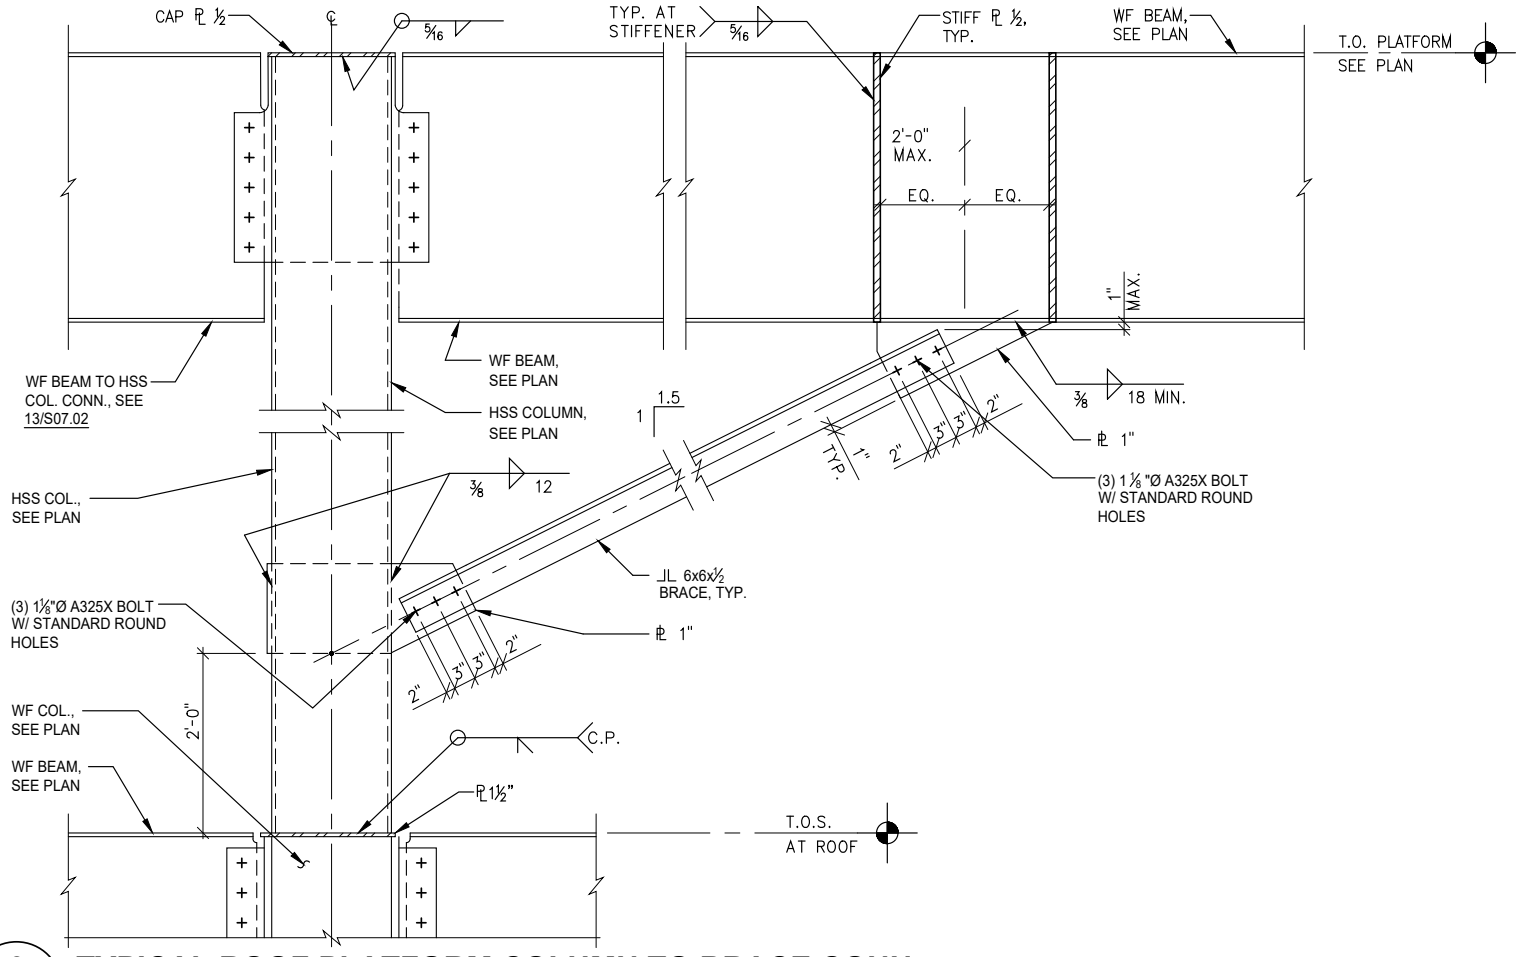



# 6 - TYPICAL ROOF PLATFORM COLUMN TO BRACE CONN.

¾" = 1'-0"